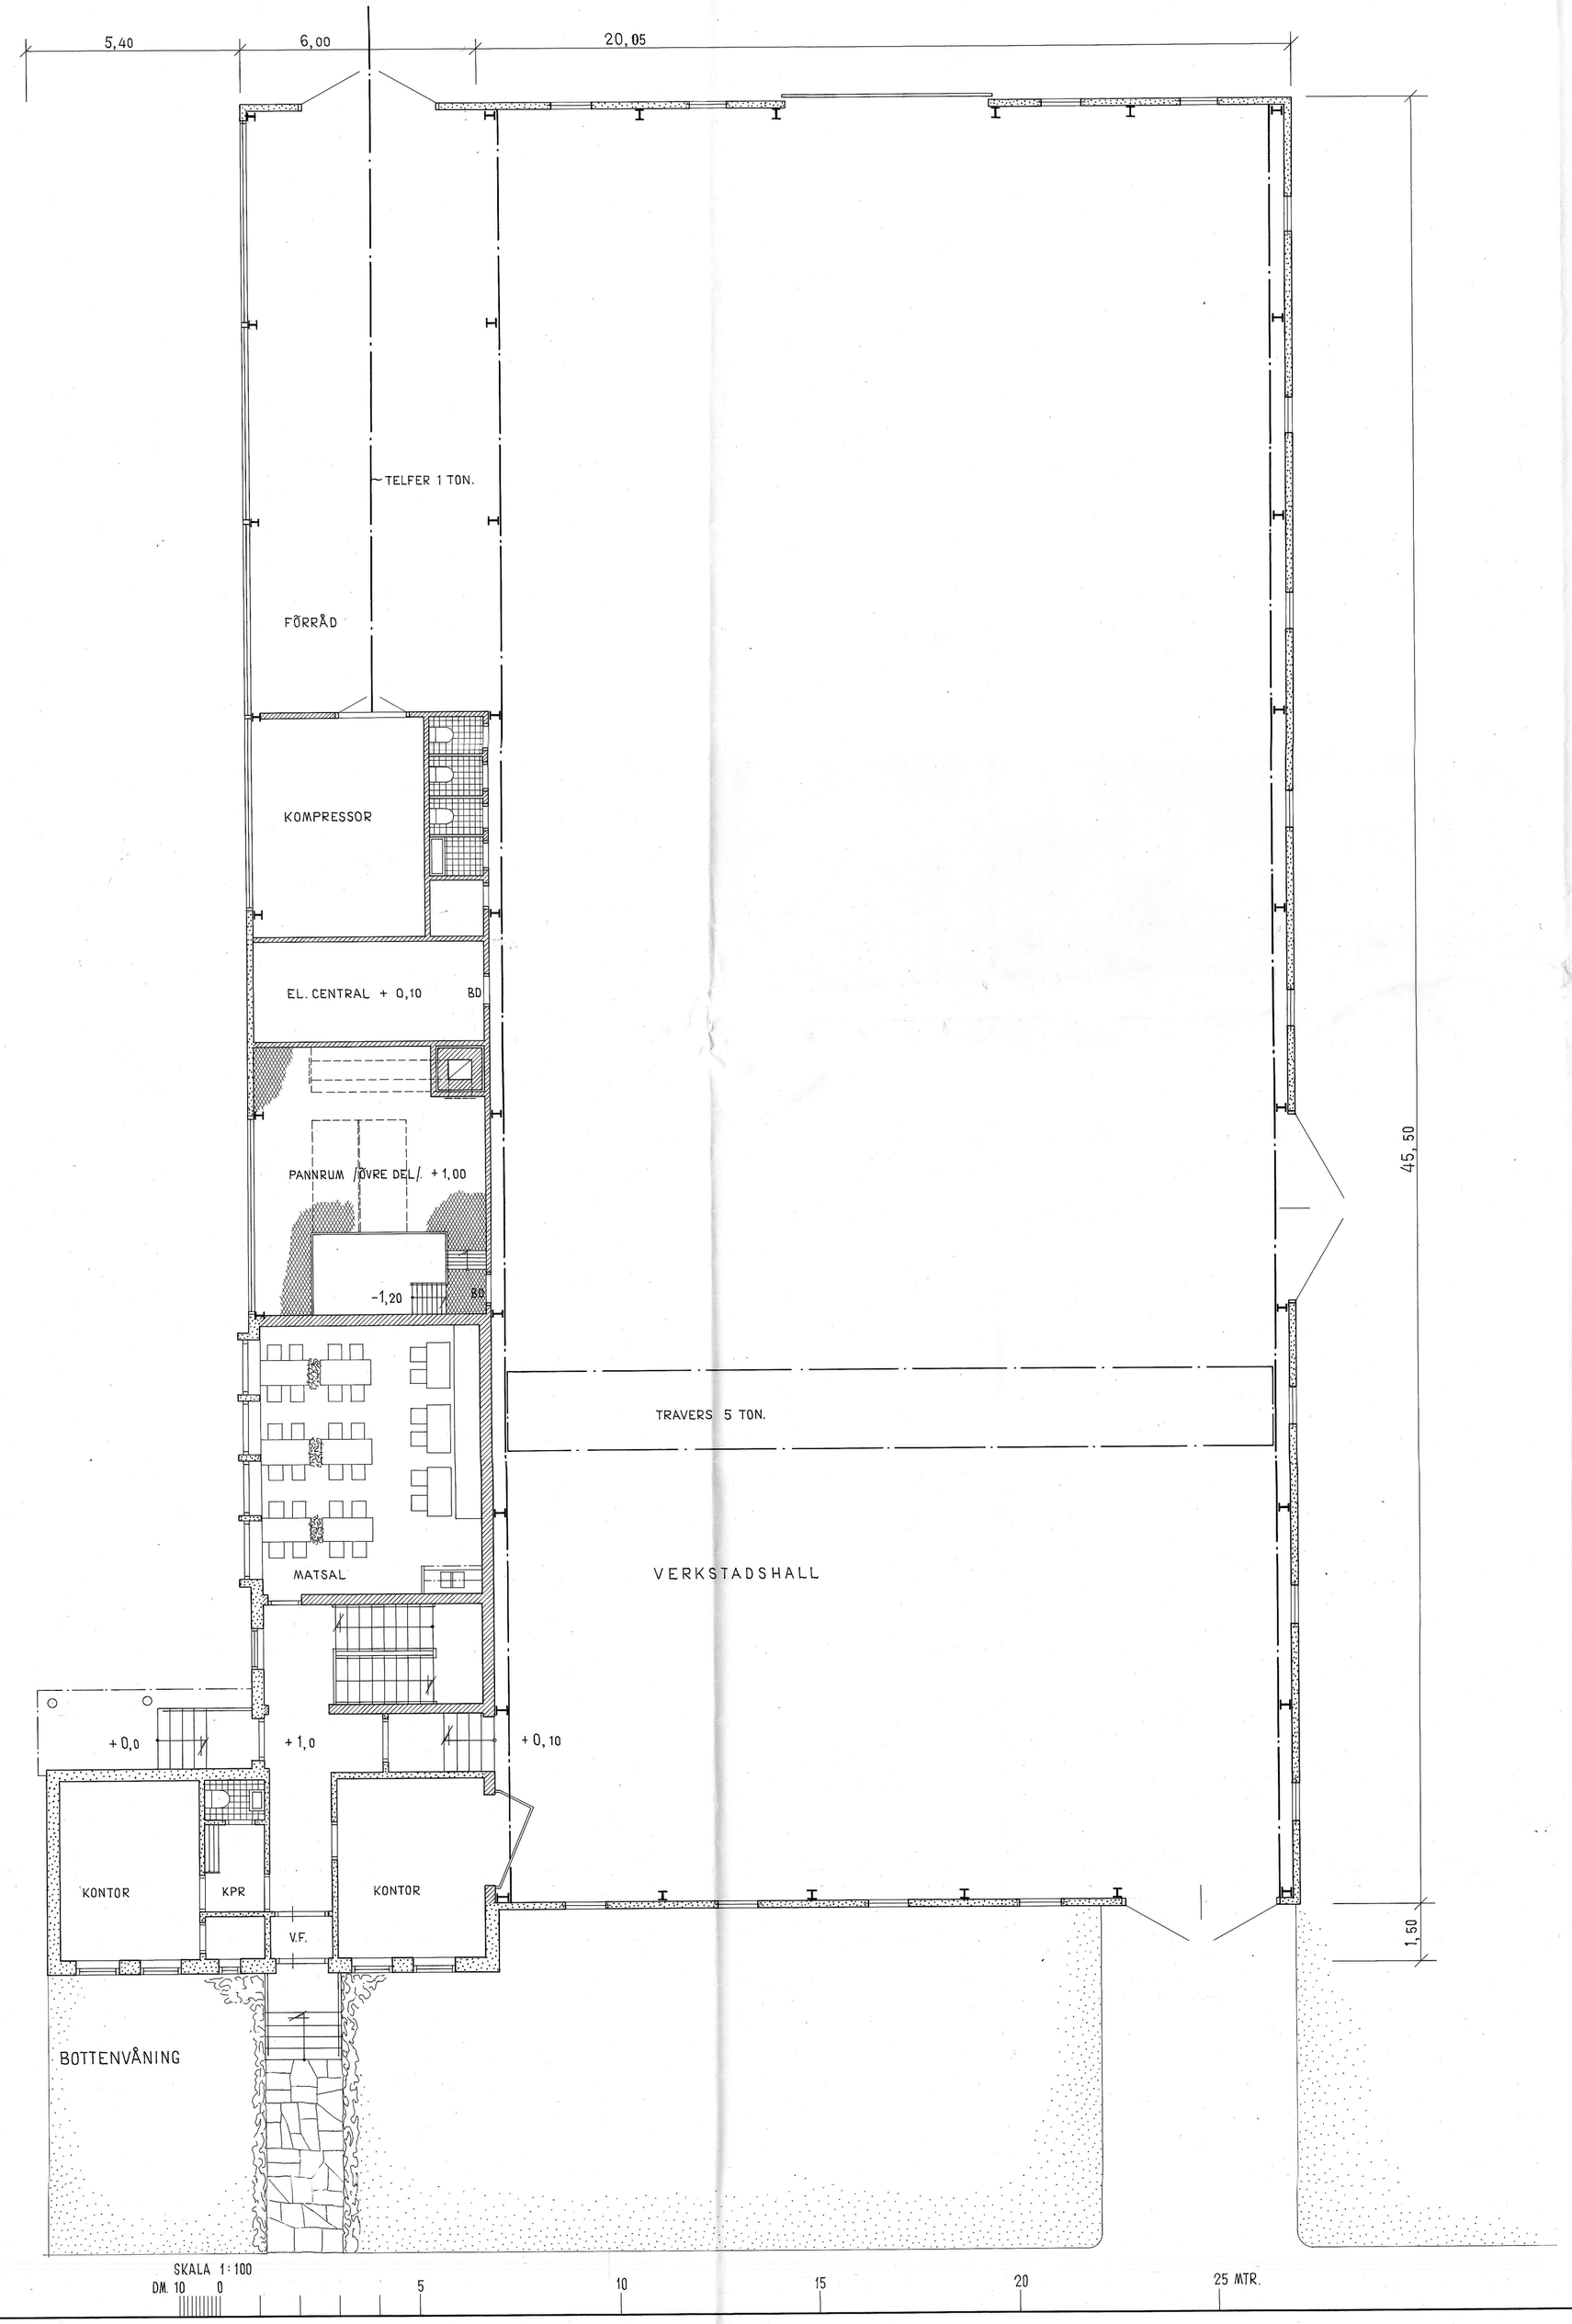

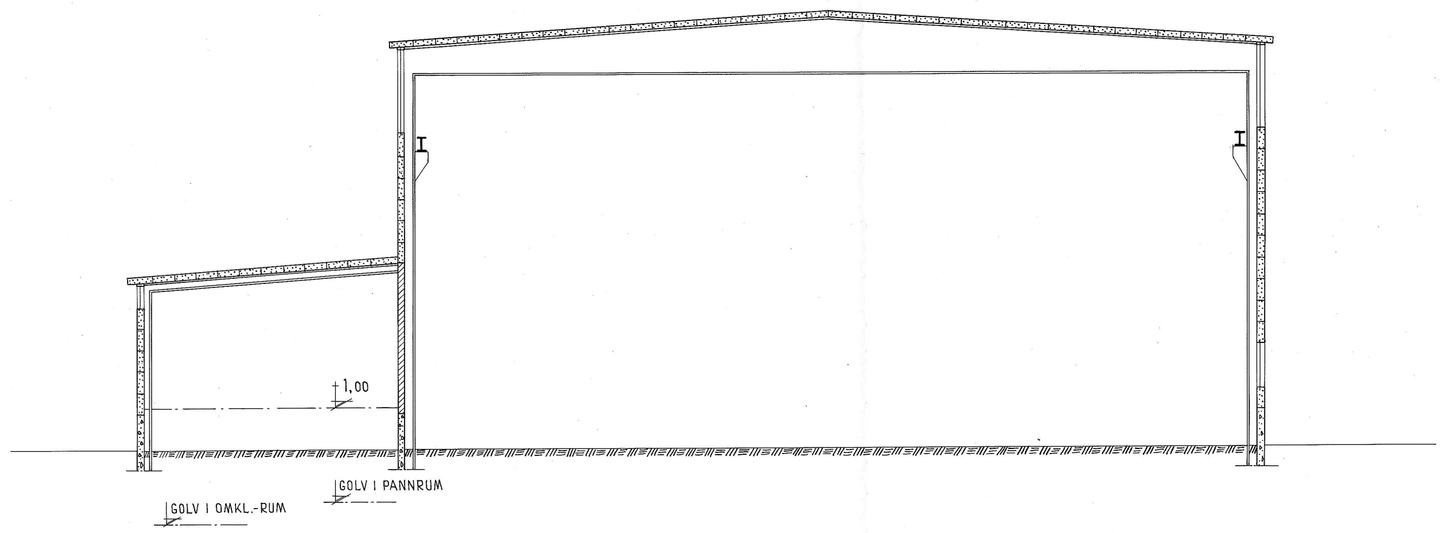

TVÄRSEKTION

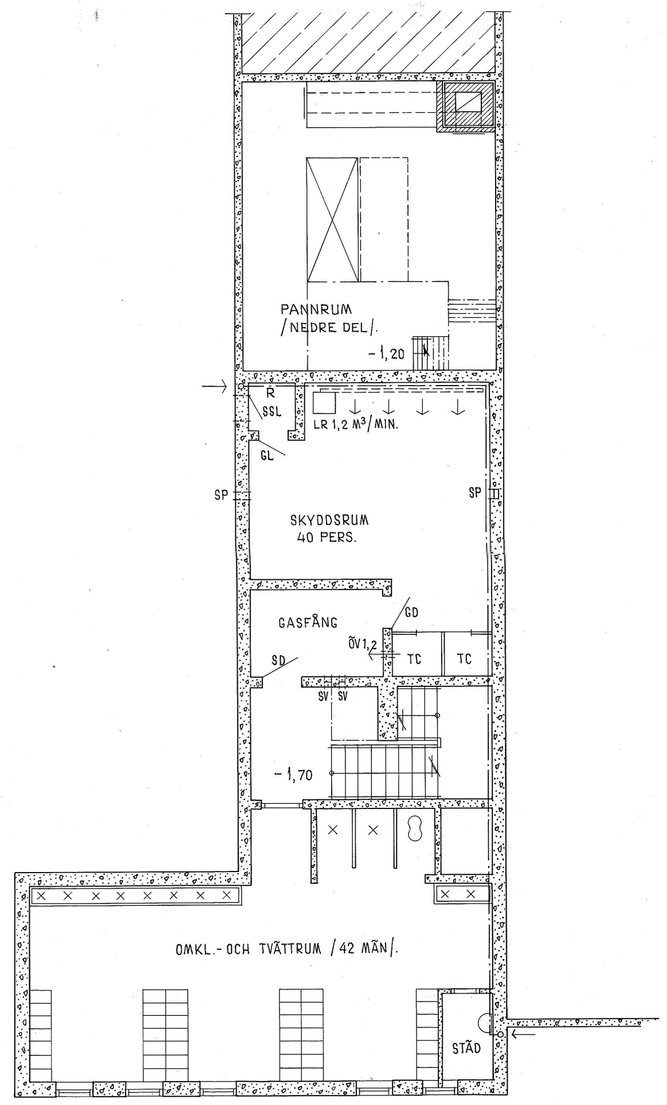

KÄLLARVÅNING

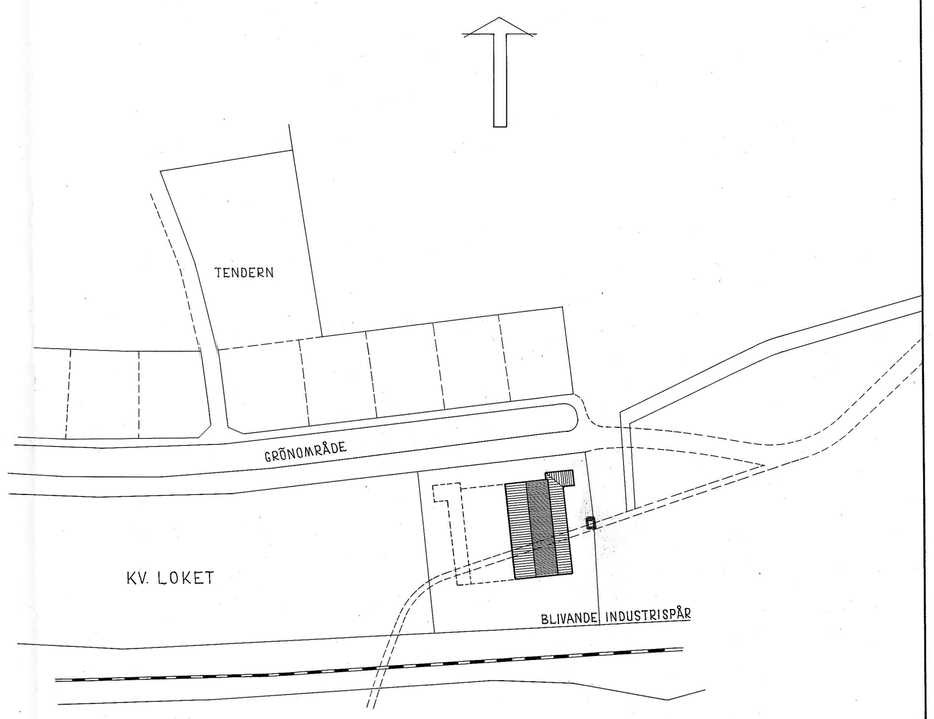

SITUATIONSPLAN
SKALA 1:2000

LITT	ÄNDRINGAR		DATUM	SIGN
KV. LOKET – KRYLBO		SKALA	1/100 – 1/2000	
NYBYGGNAD FÖR AB. AXEL G. JANSSON STOCKHOLM		MATT		
		RITAD	Ö.m.	
		KONSTR.		
BOTTENV., KÄLLARVÅN., SEKTION, SIT.-PLAN		Nr	57022 – 1	
INGENJÖRSFIRMAN JACOBSON & WIDMARK AB FOLKE JACOBSON TORSVIKSSVÄNGEN 7 A, LIDINGÖ, TEL. 65 26 40		LIDINGÖ DEN	4 MARS 1957. Folke Jacobson	